



Log of Borehole: BH1(MW)

Sheet: 1 of 1

82 Healey Road,
Bolton, ON

Project #: 25-14596

G.S.Elevation:

Location: 16m South of SBL, 8m West of EBL

Drill Method: D-50 Truck, Solid Stem

Drilling Date: 25 March 2025

Sample Method: Split Spoon


Water Level Date: 27 March 2025

Borehole Diameter: 150mm

Water Level: Dry

Logged By: T.B.

Checked By: T.B.

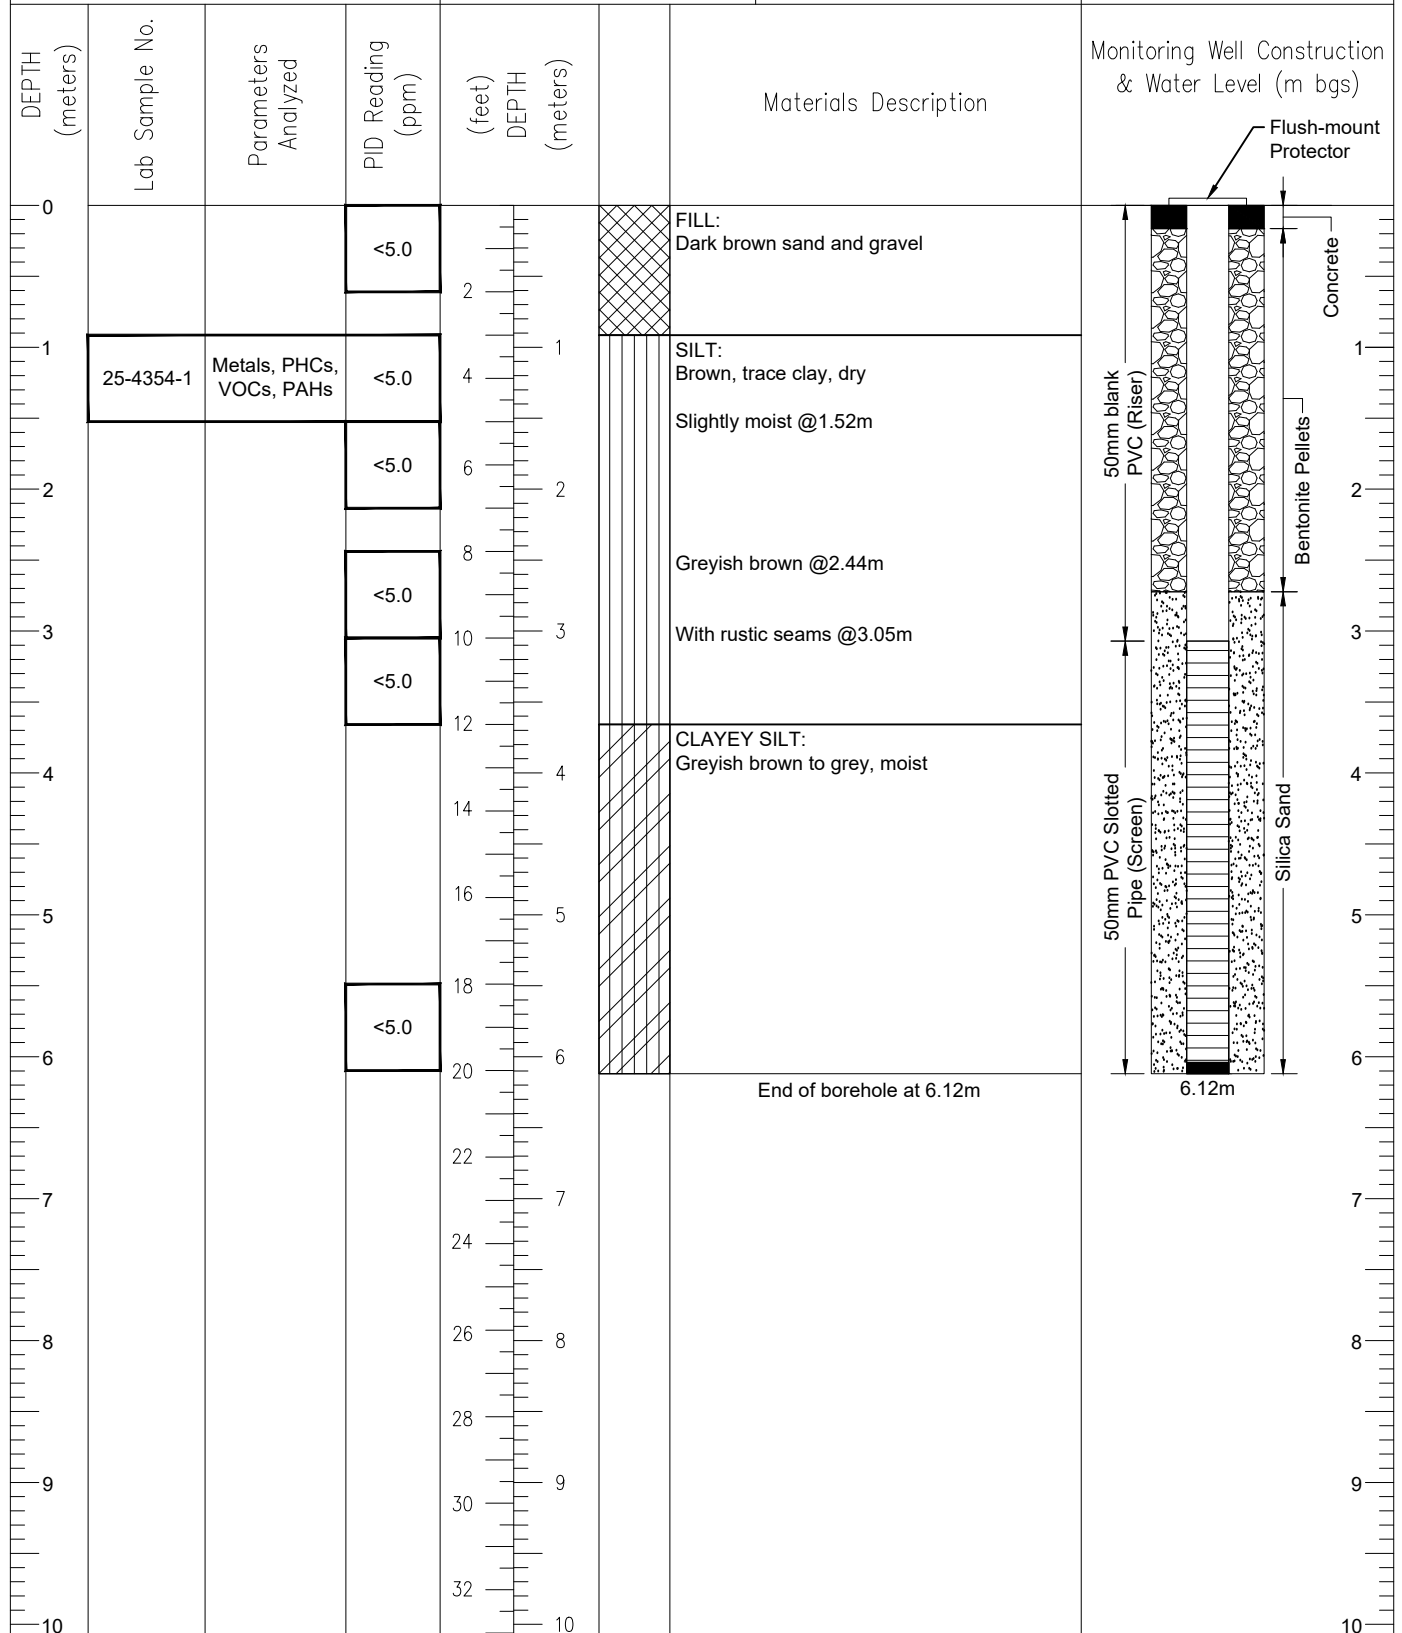



Log of Borehole: BH2

Sheet: 1 of 1

82 Healey Road,
Bolton, ON

Project #: 25-14596

G.S.Elevation:

Location: 10m East of WBL, 4m South of SBL

Drill Method: D-50 Truck, Solid Stem

Drilling Date: 25 March 2025

Sample Method: Split Spoon

Water Level Date: N/A

Borehole Diameter: 150mm

Water Level: N/A

Logged By: T.B.

Checked By: T.B.

DEPTH (meters)	Lab Sample No.	Parameters Analyzed	PID Reading (ppm)	(feet) DEPTH (meters)	Materials Description	Monitoring Well Construction & Water Level (m bgs)
0					50mm ASPHALT	
			<5.0	2	FILL: Dark brown sand and gravel, pieces of red brick	
1	25-4354-2	Metals, PHCs, VOCs, pH	<5.0	4	SILT: Brown, slightly moist	1
2			<5.0	6		2
			<5.0	8		
3			<5.0	10		3
			<5.0	12		
4				14	End of borehole at 3.66m	4
5				16		5
				18		
6				20		6
				22		
7				24		7
				26		
8				28		8
				30		
9				32		9
10						10



Log of Borehole: BH3(MW)

Sheet: 1 of 1

82 Healey Road,
Bolton, ON

Project #: 25-14596

G.S.Elevation:

Location: 4m West of WBL, 1m South of NBL

Drill Method: D-50 Truck, Solid Stem

Drilling Date: 25 March 2025

Sample Method: Split Spoon


Water Level Date: 27 March 2025

Borehole Diameter: 150mm

Water Level: 4.80m

Logged By: T.B.

Checked By: T.B.

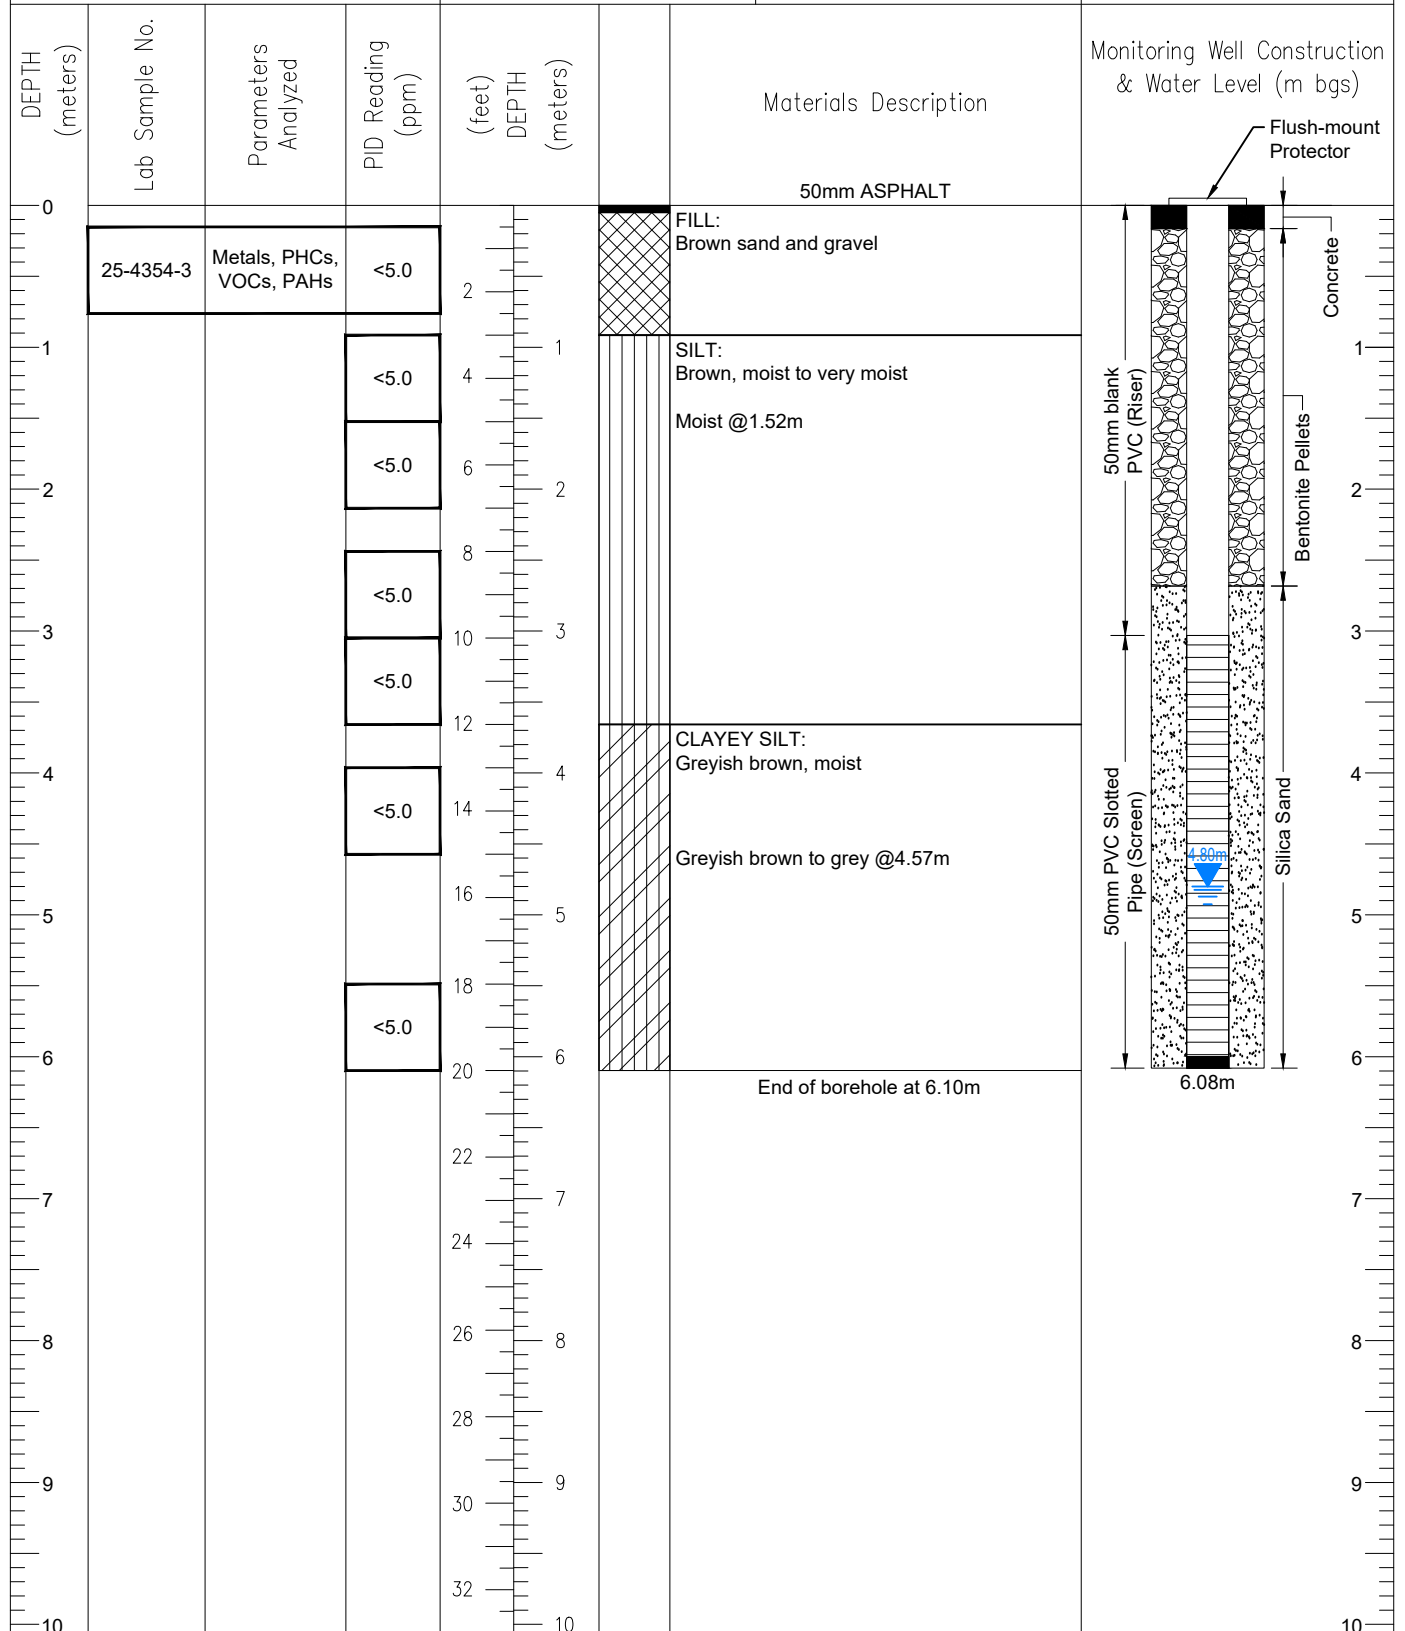



Log of Borehole: BH4(MW)

Sheet: 1 of 1

82 Healey Road,
Bolton, ON

Project #: 25-14596

G.S.Elevation:

Location: 12m East of WPL, 22m North of SPL

Drill Method: D-50 Truck, Solid Stem

Drilling Date: 25 March 2025

Sample Method: Split Spoon


Water Level Date: 27 March 2025

Borehole Diameter: 150mm

Water Level: 2.15m

Logged By: T.B.

Checked By: T.B.

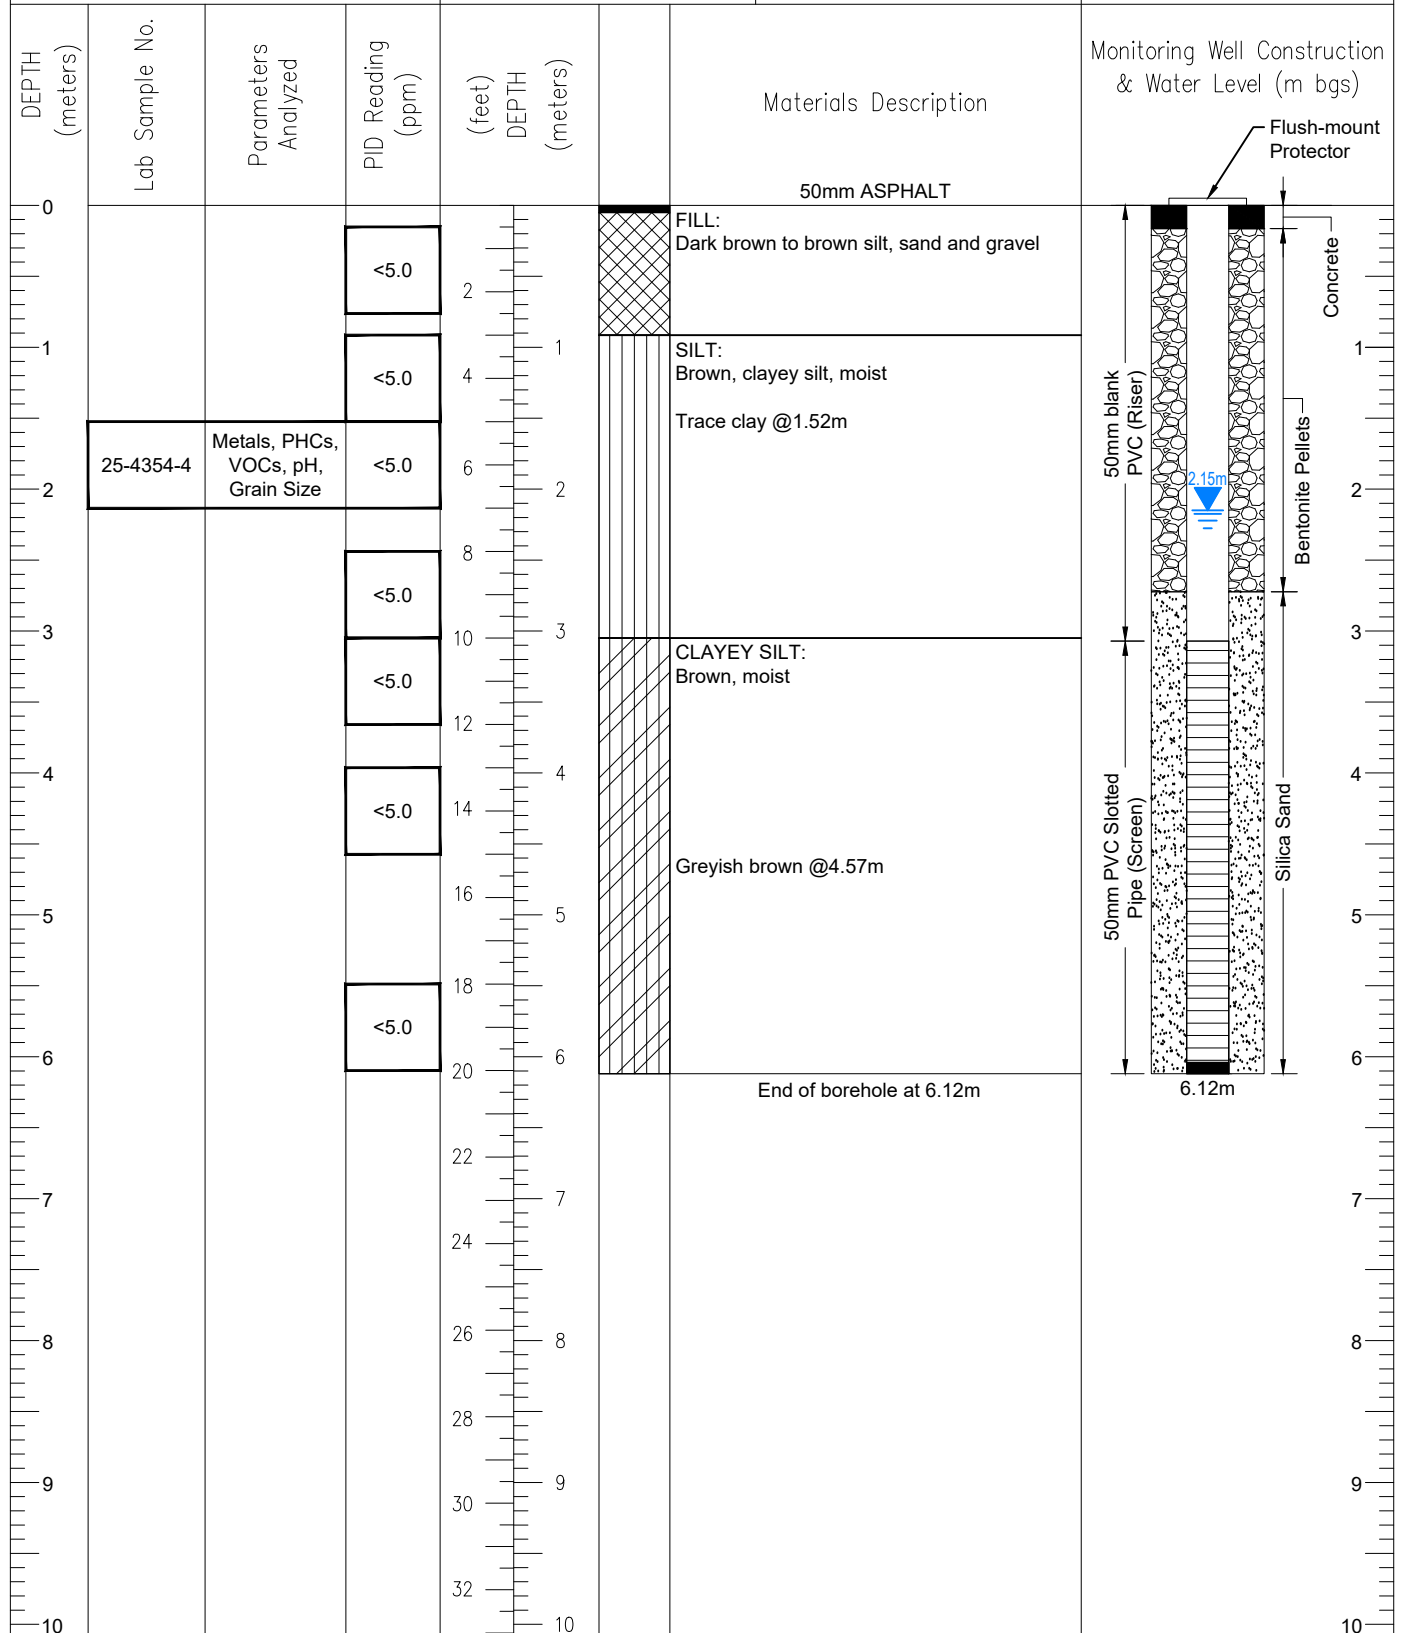



Log of Borehole: BH5

Sheet: 1 of 1

82 Healey Road,
Bolton, ON

Project #: 25-14596

G.S.Elevation:

Location: 6m West of WBL, 4m North of SPL

Drill Method: D-50 Truck, Solid Stem

Drilling Date: 25 March 2025

Sample Method: Split Spoon


Water Level Date: N/A

Borehole Diameter: 150mm

Water Level: N/A

Logged By: T.B.

Checked By: T.B.

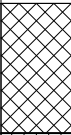DEPTH (meters)	Lab Sample No.	Parameters Analyzed	PID Reading (ppm)	(feet) DEPTH (meters)	Materials Description	Monitoring Well Construction & Water Level (m bgs)
0			<5.0	2	 FILL: Brown sand and gravel, some silt	
1	25-4354-5	Metals, PHCs, VOCs	<5.0	4	 SILT: Brown, slightly moist	1
2			<5.0	6		2
			<5.0	8		
3			<5.0	10	Moist @2.44m	3
			<5.0	12		
4				14	End of borehole at 3.66m	4
5				16		5
6				18		6
7				20		7
8				22		8
9				24		9
10				26		10